BTN설법학교 대웅전 신축 계획(안)

기획설계 도면 — 건축사무소 설계 의뢰용


건물명	대웅전 (현판명: BTN설법학교)
용도	종교시설(사찰 법당) — 예불 · 설법 강의 · 방송 녹화/중계
구조	전통 한식 목구조 (육송 기준), 장대석 기단, 초석 위 원기둥
규모	지상 1층 / 정면 5칸 × 측면 4칸
주칸	정면 3.6 + 4.2 + 4.8 + 4.2 + 3.6 = 20.4m ｜ 측면 3.0 + 4.2 + 4.2 + 3.0 = 14.4m
바닥면적	293.76㎡ (88.9평) — 기둥 중심선 기준
기단면적	407.16㎡ (123.2평) — 기단 23.4 × 17.4m
높이	기단 0.9m / 마루 FL+1.5m / 반자 +8.25m / 최고 약 12.6m (취두)
지붕·공포	팔작지붕, 한식 기와 / 다포식 공포, 처마 내밀기 2.6m
수용	좌식 방석 약 124석 (의자 배치 시 약 74석)
특화	감주법(어칸 내고주 생략)으로 시야 확보, 방송조명 배턴 3열, 카메라 4포지션, 마루 하부 배선, 중계연결반(TP), 중계차 외부 접속

도면 목록

A-000	표지 · 설계개요	-
A-001	배치도(개념)	1:400
A-101	평면도	1:100
A-102	방송·조명 설비 계획도	1:100
A-201	정면도	1:100
A-202	측면도	1:100
A-301	횡단면도	1:100
A-901	설계의뢰 체크리스트	-

기획 의도 (PD 노트)

· '설법학교' — 법당이 곧 강의실이자 스튜디오. 예불 공간의 위엄은 지키되, 강의·녹화가 매주 돌아가는 '운영 가능한 법당'이 목표.
· 화면의 주인공은 불단과 법사. 정면 카메라(C1) 축선에 기둥이 걸리지 않도록 어칸 내고주 생략.
· 조명·전원·신호선은 보이지 않게: 반자 속 윈치, 마루 하부 배선, 후면 장비 공간으로 정리.
· 꽃살문 전면 개방 시 마당까지 이어지는 야외 대법회·중계 동선 확보.

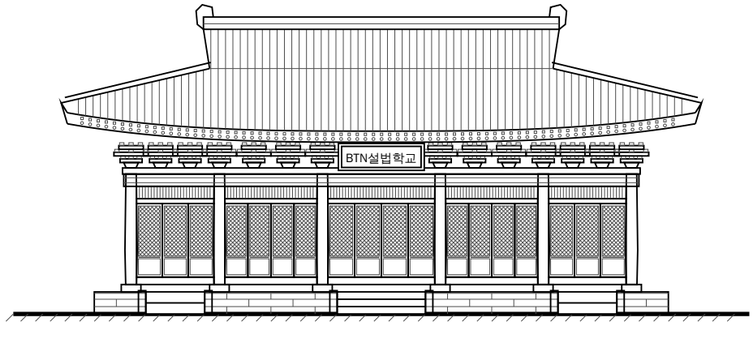


정면 개념도 (S=1:250)

비 고

1. 치수 단위 mm, 그리드는 기둥 중심선.
2. 본 도면은 발주자의 공간·규모·용도 의도를 전달하는 기획 단계 계획안임.
3. 구조·법규·인허가·문화재 심의 검토 및 실시설계는 건축사무소에서 수행.

프로젝트	BTN설법학교 대웅전 신축 계획(안)
현판명	BTN설법학교
발주(사찰)	(기입)
설계단계	기획설계(안) — 시공용 아님
도면명	표지 · 설계개요
도면번호	A-000
축척	NONE
작성일	2026.11.12
작성	발주자 기획안 (PD 검토용)

건축사무소 검토 / 날인

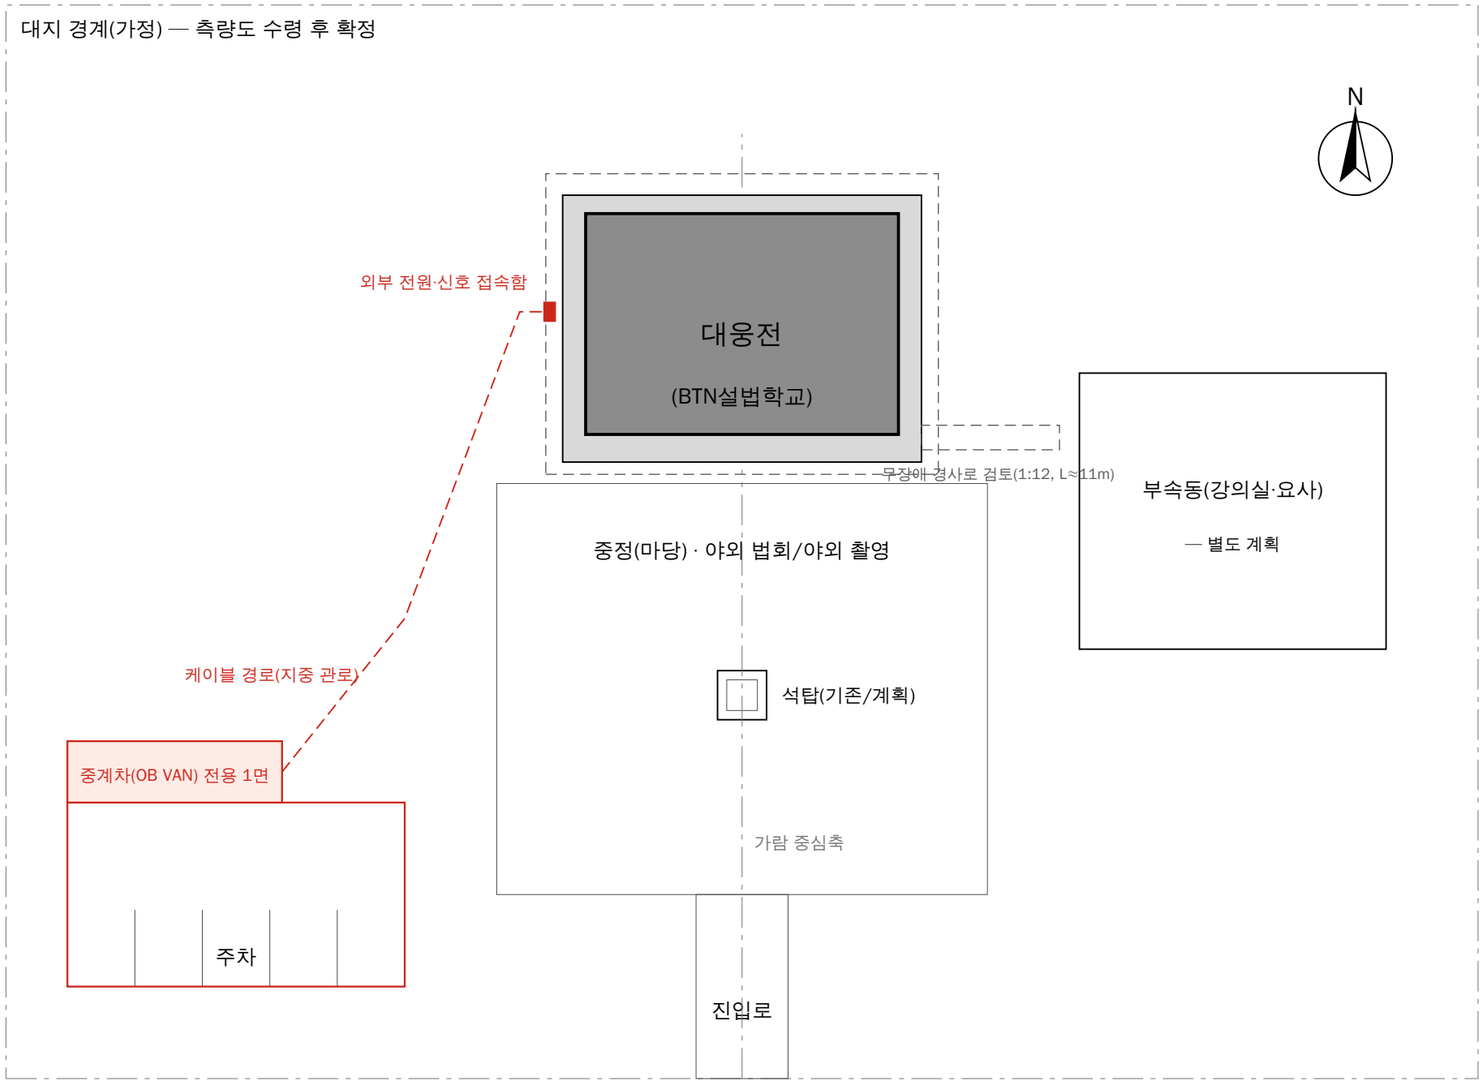

배치도(개념) S = 1:400


0 5 10 20 30 m

비 고

1. 치수 단위 mm, 그리드는 기둥 중심선.
2. 본 도면은 발주자의 공간·규모·용도 의도를 전달하는 기획 단계 계획안임.
3. 구조·법규·인허가·문화재 심의 검토 및 실시설계는 건축사무소에서 수행.
4. 대지 형상·방위·주변 건물은 가정임.
5. 중계차 동선·외부 접속함 위치 확인.

프로젝트	BTN설법학교 대웅전 신축 계획(안)
현판명	BTN설법학교
발주(사찰)	(기입)
설계단계	기획설계(안) — 시공용 아님
도면명	배치도(개념)
도면번호	A-001
축척	1:400 (A3)
작성일	2026.11.12
작성	발주자 기획안 (PD 검토용)

건축사무소 검토 / 날인

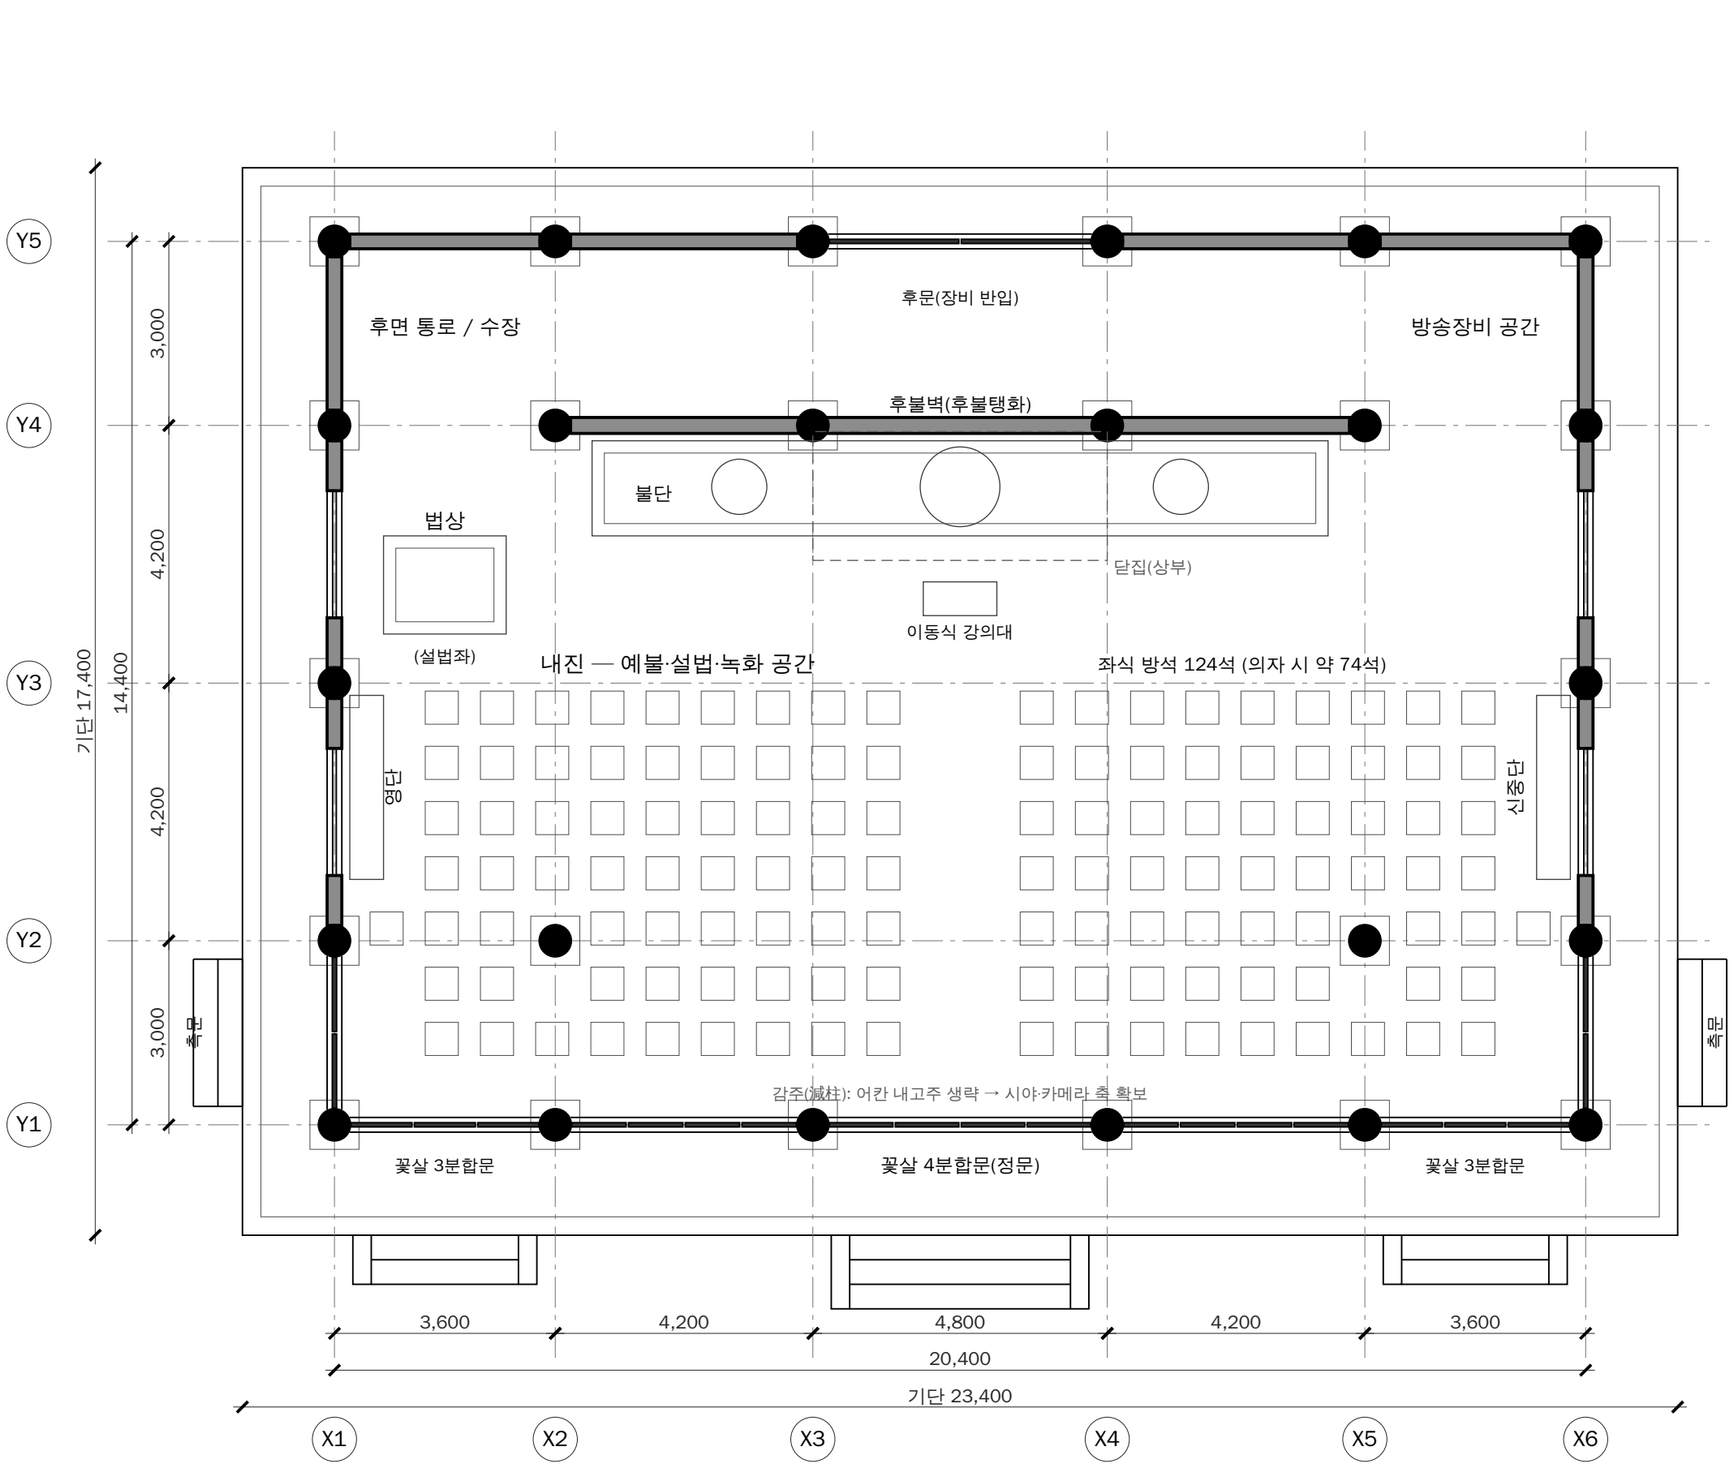

평면도 S = 1:100


0 1 2 5 10 m

비 고

1. 치수 단위 mm, 그리드는 기둥 중심선.
2. 본 도면은 발주자의 공간·규모·용도 의도를 전달하는 기획 단계 계획안임.
3. 구조·법규·인허가·문화재 심의 검토 및 실시설계는 건축사무소에서 수행.
4. 어칸 전면 내고주 2본 감주(減柱).
5. 불단·법상·의례단 위치는 협의 후 확정.
6. 좌식 방석 0.9×0.9m 피치, 124석.

프로젝트	BTN설법학교 대웅전 신축 계획(안)
현판명	BTN설법학교
발주(사찰)	(기입)
설계단계	기획설계(안) — 시공용 아님
도면명	평면도
도면번호	A-101
축척	1:100 (A3)
작성일	2026.11.12
작성	발주자 기획안 (PD 검토용)

건축사무소 검토 / 날인

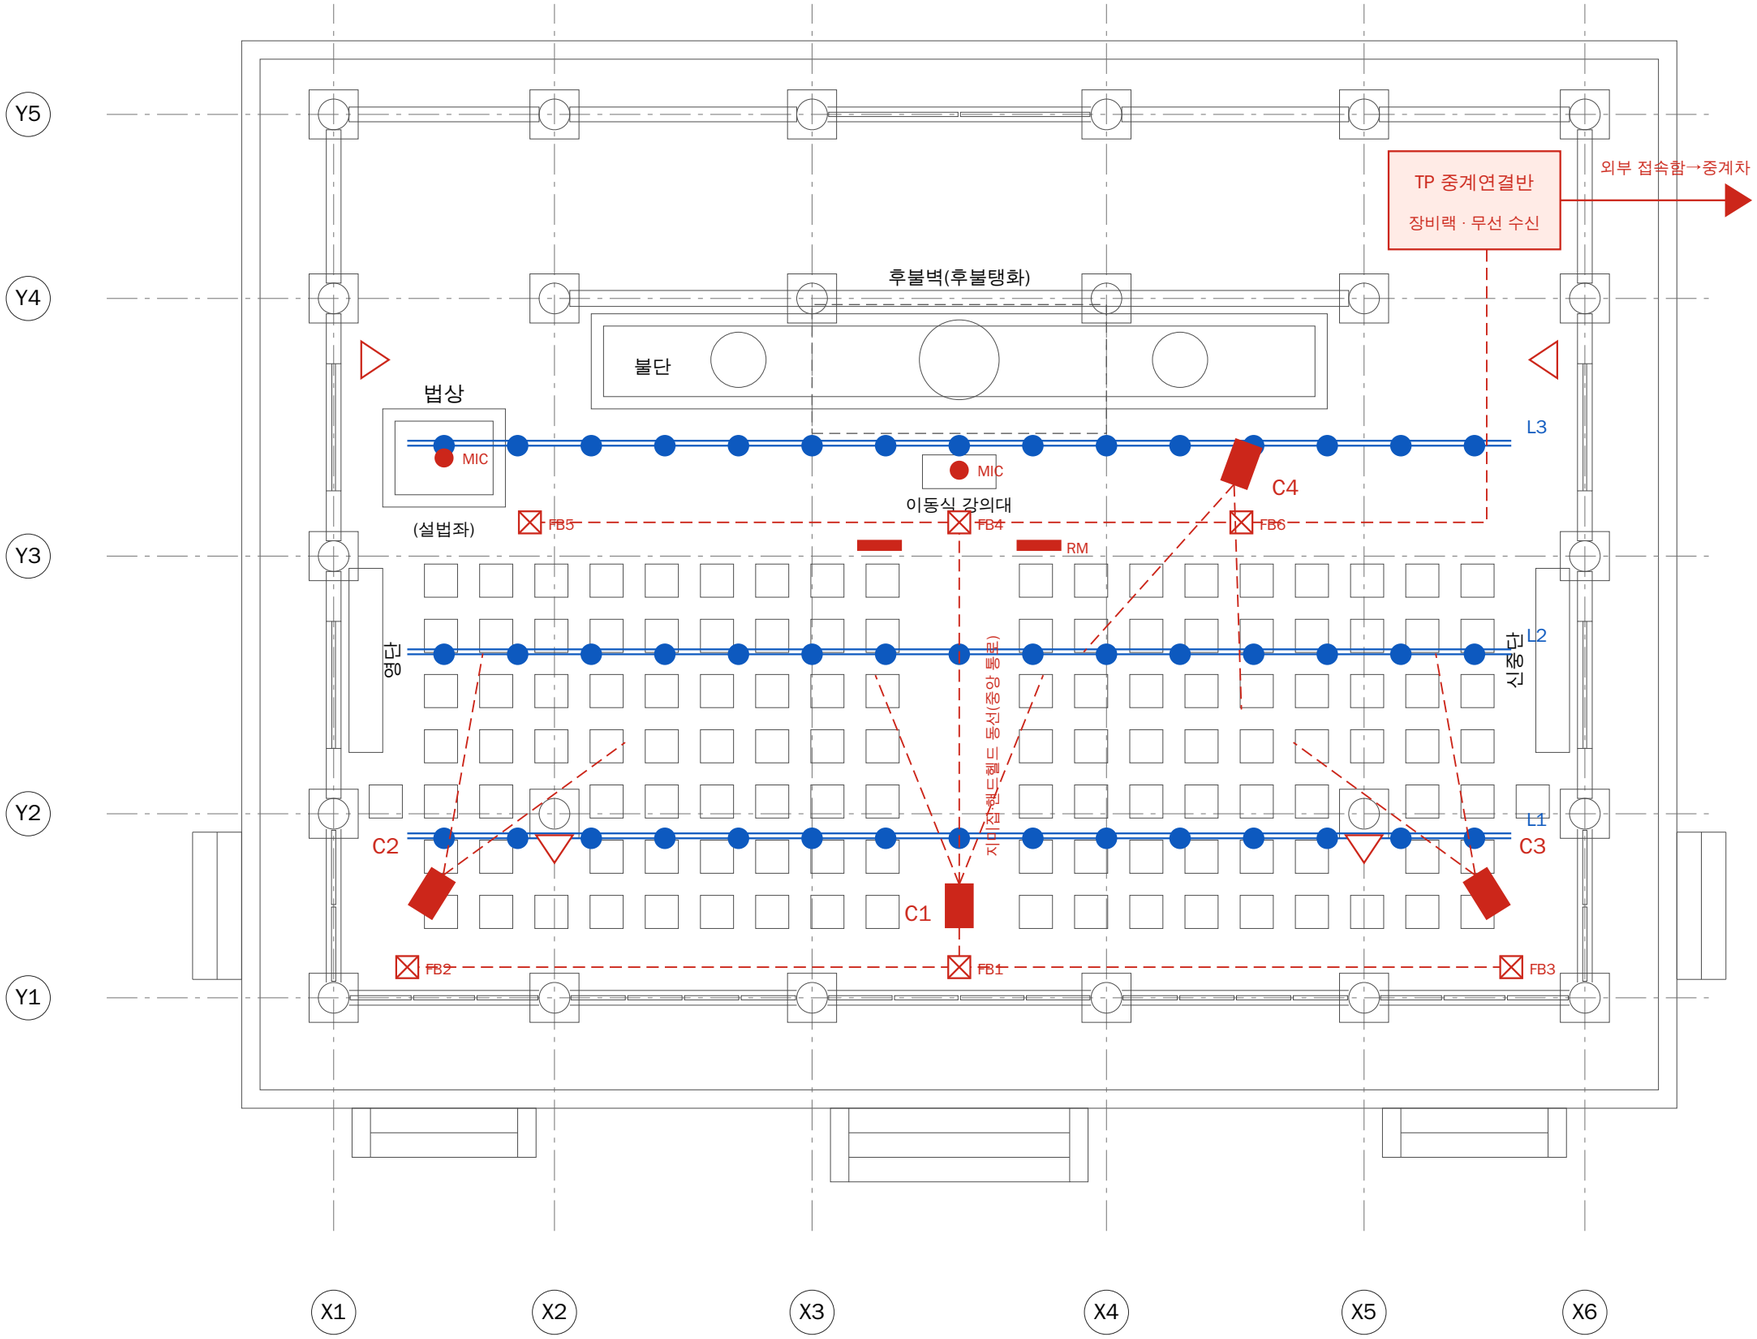

방송·조명 설비 계획도 S = 1:100

0 1 2 5 10 m

비 고


1. 치수 단위 mm, 그리드는 기둥 중심선.
2. 본 도면은 발주자의 공간·규모·용도 의도를 전달하는 기획 단계 계획안임.
3. 구조·법규·인허가·문화재 심의 검토 및 실시설계는 건축사무소에서 수행.
4. 방송설비는 운영 요구사항이며, 상세는 방송·전기 설계자와 협의.
5. 조명 배턴: 우물반자 내 전동 윈치 하강식. L1 전면 키 / L2 청중·보조 / L3 강단 역광·탑.
6. 카메라: C1 메인 정면(어칸 축), C2·C3 좌우 사선, C4 리버스(청중).
7. 케이블은 전부 마루 하부 은폐.
8. RM: 법사용 리턴모니터·프롬프터.
9. TP 중계연결반 ↔ 외부 접속함 ↔ 중계차(배치도 A-001 참조).

범 례

- 카메라 포지션(C1~C4)
- 방송조명 배턴(L1~L3)
- 마루 하부 케이블 경로
- 바닥 매립 박스(FB)
- 스피커(SP)
- 마이크 단자(MIC)

프로젝트	BTN설법학교 대웅전 신축 계획(안)
현판명	BTN설법학교
발주(사찰)	(기입)
설계단계	기획설계(안) — 시공용 아님
도면명	방송·조명 설비 계획도
도면번호	A-102
축척	1:100 (A3)
작성일	2026.11.12
작성	발주자 기획안 (PD 검토용)

건축사무소 검토 / 날인

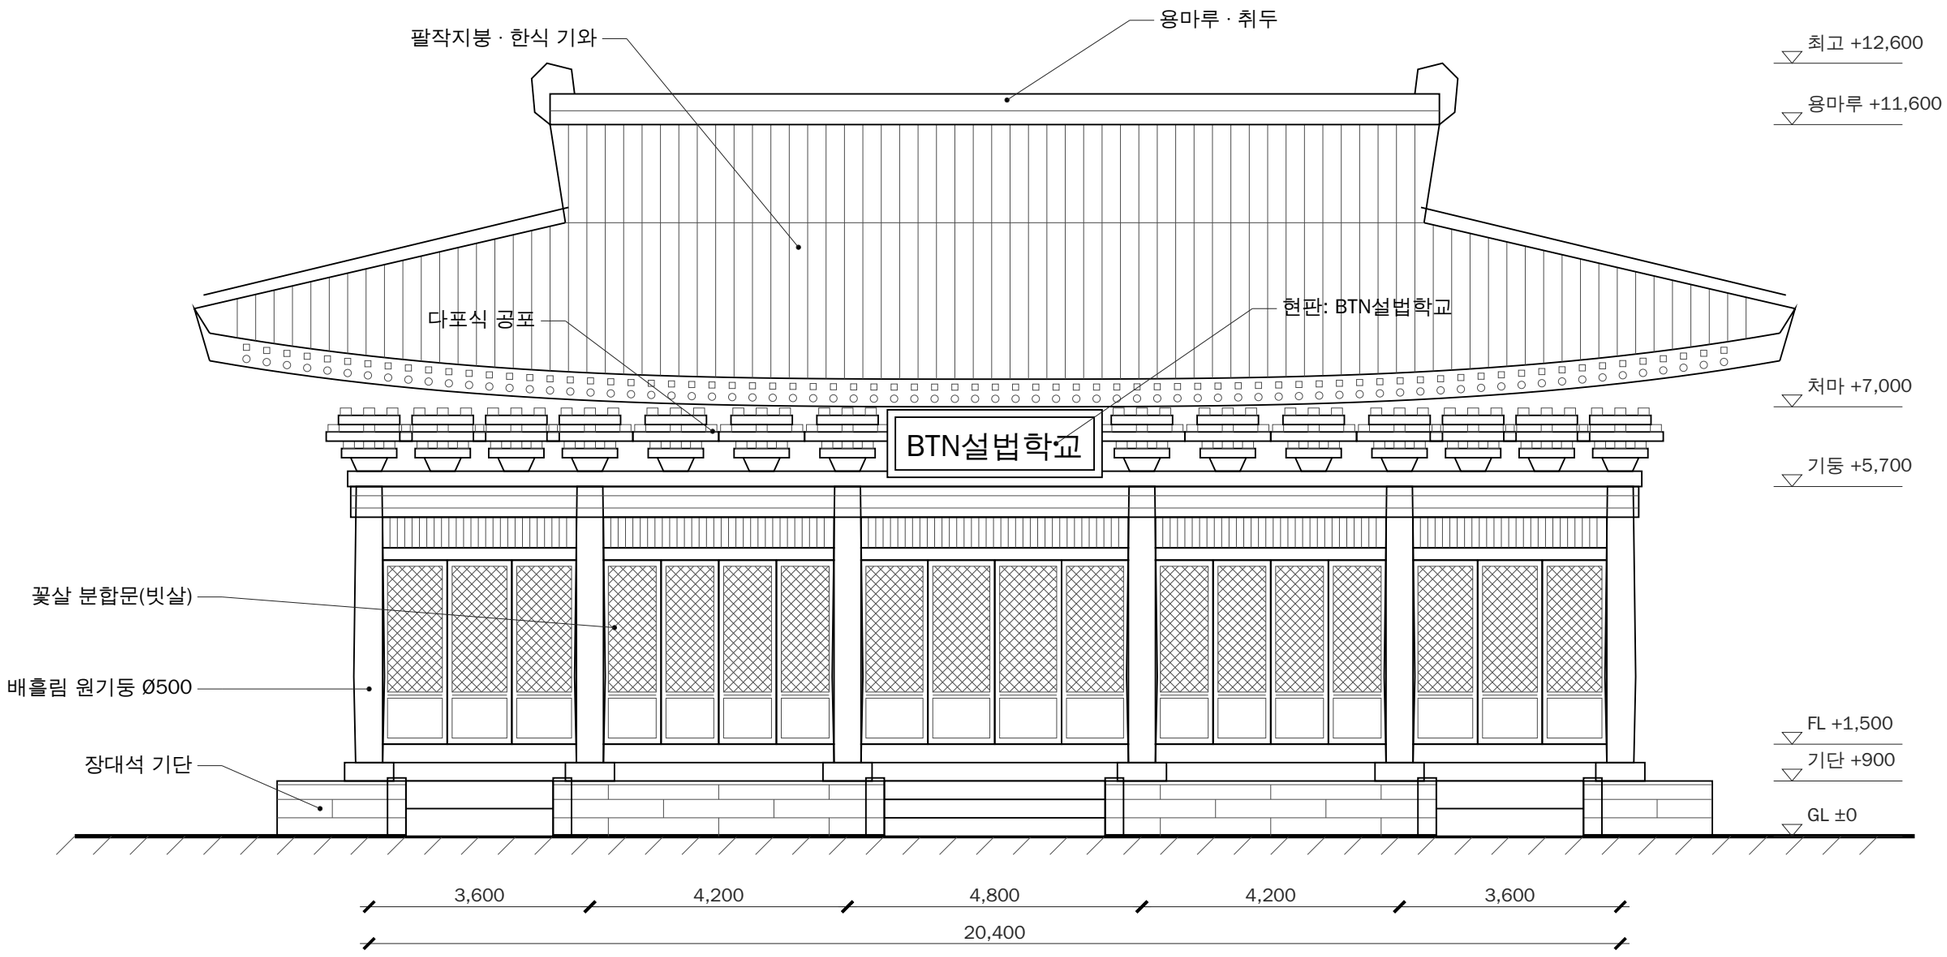

정면도 S = 1:100


0 1 2 5 10 m

비 고

1. 치수 단위 mm, 그리드는 기둥 중심선.
2. 본 도면은 발주자의 공간·규모·용도 의도를 전달하는 기획 단계 계획안임.
3. 구조·법규·인허가·문화재 심의 검토 및 실시설계는 건축사무소에서 수행.
4. 배면도는 정면도 준용(어칸 후문).
5. 앙곡·안허리곡 등 처마 곡은 개념 표현이며 실시설계 시 결정.
6. 현판 서체·크기는 별도 협의.

프로젝트	BTN설법학교 대웅전 신축 계획(안)
현판명	BTN설법학교
발주(사찰)	(기입)
설계단계	기획설계(안) — 시공용 아님
도면명	정면도
도면번호	A-201
축척	1:100 (A3)
작성일	2026.11.12
작성	발주자 기획안 (PD 검토용)

건축사무소 검토 / 날인

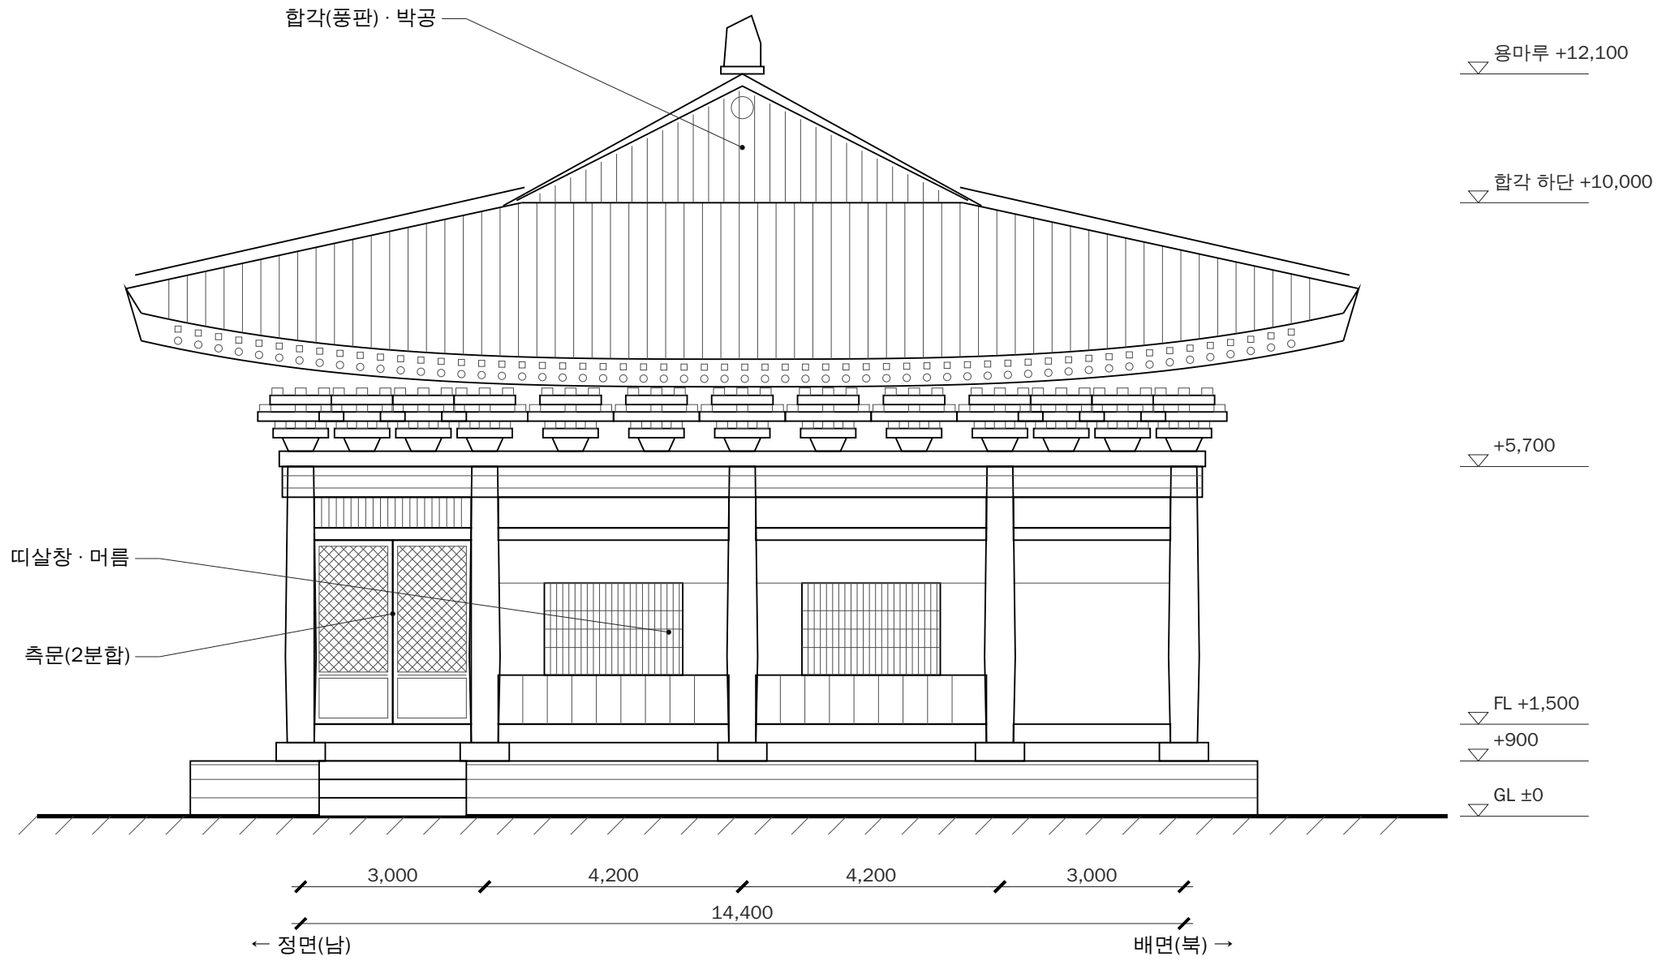

측면도(동측) S = 1:100


0 1 2 5 10 m

비 고

1. 치수 단위 mm, 그리드는 기둥 중심선.
2. 본 도면은 발주자의 공간·규모·용도 의도를 전달하는 기획 단계 계획안임.
3. 구조·법규·인허가·문화재 심의 검토 및 실시설계는 건축사무소에서 수행.
4. 동측면 기준, 서측면은 대칭.
5. 측문 전면 소형 계단 설치.

프로젝트	BTN설법학교 대웅전 신축 계획(안)
현판명	BTN설법학교
발주(사찰)	(기입)
설계단계	기획설계(안) — 시공용 아님
도면명	측면도
도면번호	A-202
축척	1:100 (A3)
작성일	2026.11.12
작성	발주자 기획안 (PD 검토용)

건축사무소 검토 / 날인

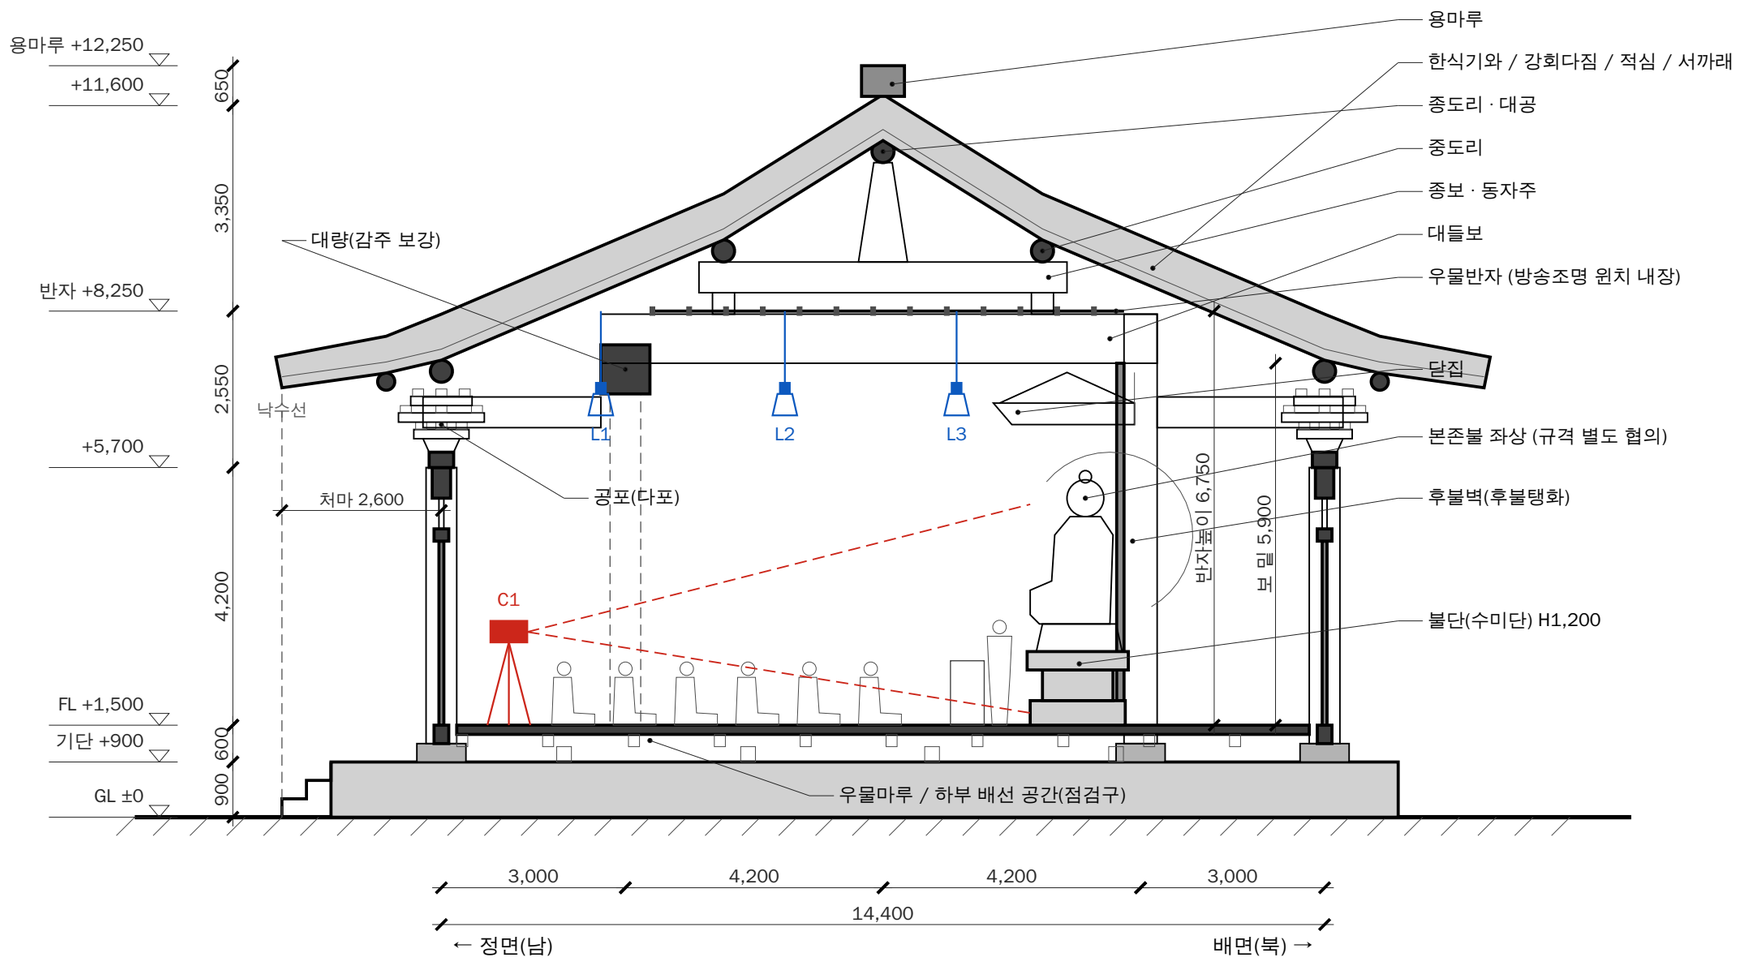

횡단면도 S = 1:100

0 1 2 5 10 m

비 고

1. 치수 단위 mm, 그리드는 기둥 중심선.
2. 본 도면은 발주자의 공간·규모·용도 의도를 전달하는 기획 단계 계획안임.
3. 구조·법규·인허가·문화재 심의 검토 및 실시설계는 건축사무소에서 수행.
4. 어칸 중심 절단, 서측을 바라봄.
5. 가구·부재 단면은 개념이며 구조 검토 후 확정.
6. 반자 높이 6,750(FL 기준)으로 방송조명 각도·열 배출 확보.

프로젝트	BTN설법학교 대웅전 신축 계획(안)
현판명	BTN설법학교
발주(사찰)	(기입)
설계단계	기획설계(안) — 시공용 아님
도면명	횡단면도
도면번호	A-301
축척	1:100 (A3)
작성일	2026.11.12
작성	발주자 기획안 (PD 검토용)

건축사무소 검토 / 날인

건축사무소 전달 사항 / 확정 필요 사항

A. 발주자가 제공할 자료

☐ 대지 측량도(지적·현황), 방위, 고저차
☐ 토지이용계획 / 전통사찰·문화재 보호구역 여부
☐ 기존 가람 배치도 및 사진
☐ 봉안 불상 규격(좌상 높이·폭)과 협시 구성
☐ 후불탱화·신중탱화 규격
☐ 총사업비 / 목표 준공 시점(법회 일정)

C. 건축사무소 검토 요청

☐ 감주(어칸 내고주 생략) 시 대량 단면·구조 안정성
☐ 목조 법당 화재안전: 불꽃감지기·옥외소화전·
  방수총, 목재 난연 처리, 전기 아크차단기
☐ 무장애 접근(기단 900 → 경사로 1:12) 위치
☐ 바닥 난방(마루 하부 공간과 배선 간섭)
☐ 적설·풍하중, 기와 하중 대비 가구 단면

B. 종단·스님 협의 후 확정

☐ 불단·법상·신중단·영단 위치와 의례 동선
☐ 현판 서체·글씨('BTN설법학교') 및 낙관
☐ 단청 여부와 등급(모로/금단청)
☐ 정면 칸수(5칸) · 측면 칸수(4칸) 최종 결정

D. 방송 운영 요구사항 (BTN 녹화 기준)

☐ 방송조명 전용 분전반 (LED 기준 약 15kW+예비)
☐ 조명 배턴 L1~L3 전동 윈치, 반자 내 점검 통로
☐ 마루 하부 케이블 경로 + 바닥 매립 박스 FB1~6
☐ 후면 장비 공간: 중계연결반(TP)·랙·환기
☐ 외부 접속함 ↔ 중계차 지중 관로, 차량 1면
☐ 저소음 공조(실내 NC-25 이하 목표), 잔향 검토
☐ 무대 정면 꽃살문 차광(녹화 시 암막 대응)

※ 본 패키지(PDF + DXF)는 발주자의 기획 의도 전달용입니다. DXF는 레이어별(A-*, B-*)로 정리되어
건축사무소에서 바로 기본설계의 바탕도로 쓰실 수 있습니다. 치수는 모두 스크립트 변수로 일괄 수정 가능합니다.

비 고

1. 치수 단위 mm, 그리드는 기둥 중심선.
2. 본 도면은 발주자의 공간·규모·용도
   의도를 전달하는 기획 단계 계획안임.
3. 구조·법규·인허가·문화재 심의 검토
   및 실시설계는 건축사무소에서 수행.

프로젝트	BTN설법학교 대웅전 신축 계획(안)
현판명	BTN설법학교
발주(사찰)	(기입)
설계단계	기획설계(안) — 시공용 아님
도면명	설계의뢰 체크리스트
도면번호	A-901
축척	NONE
작성일	2026.11.12
작성	발주자 기획안 (PD 검토용)

건축사무소 검토 / 날인